




REV NO. DATE 05/19/2021 REV NO. JOB NO. 21-182 CHKD BY GJB DRAWN BY REM SHEET NO. REV D2

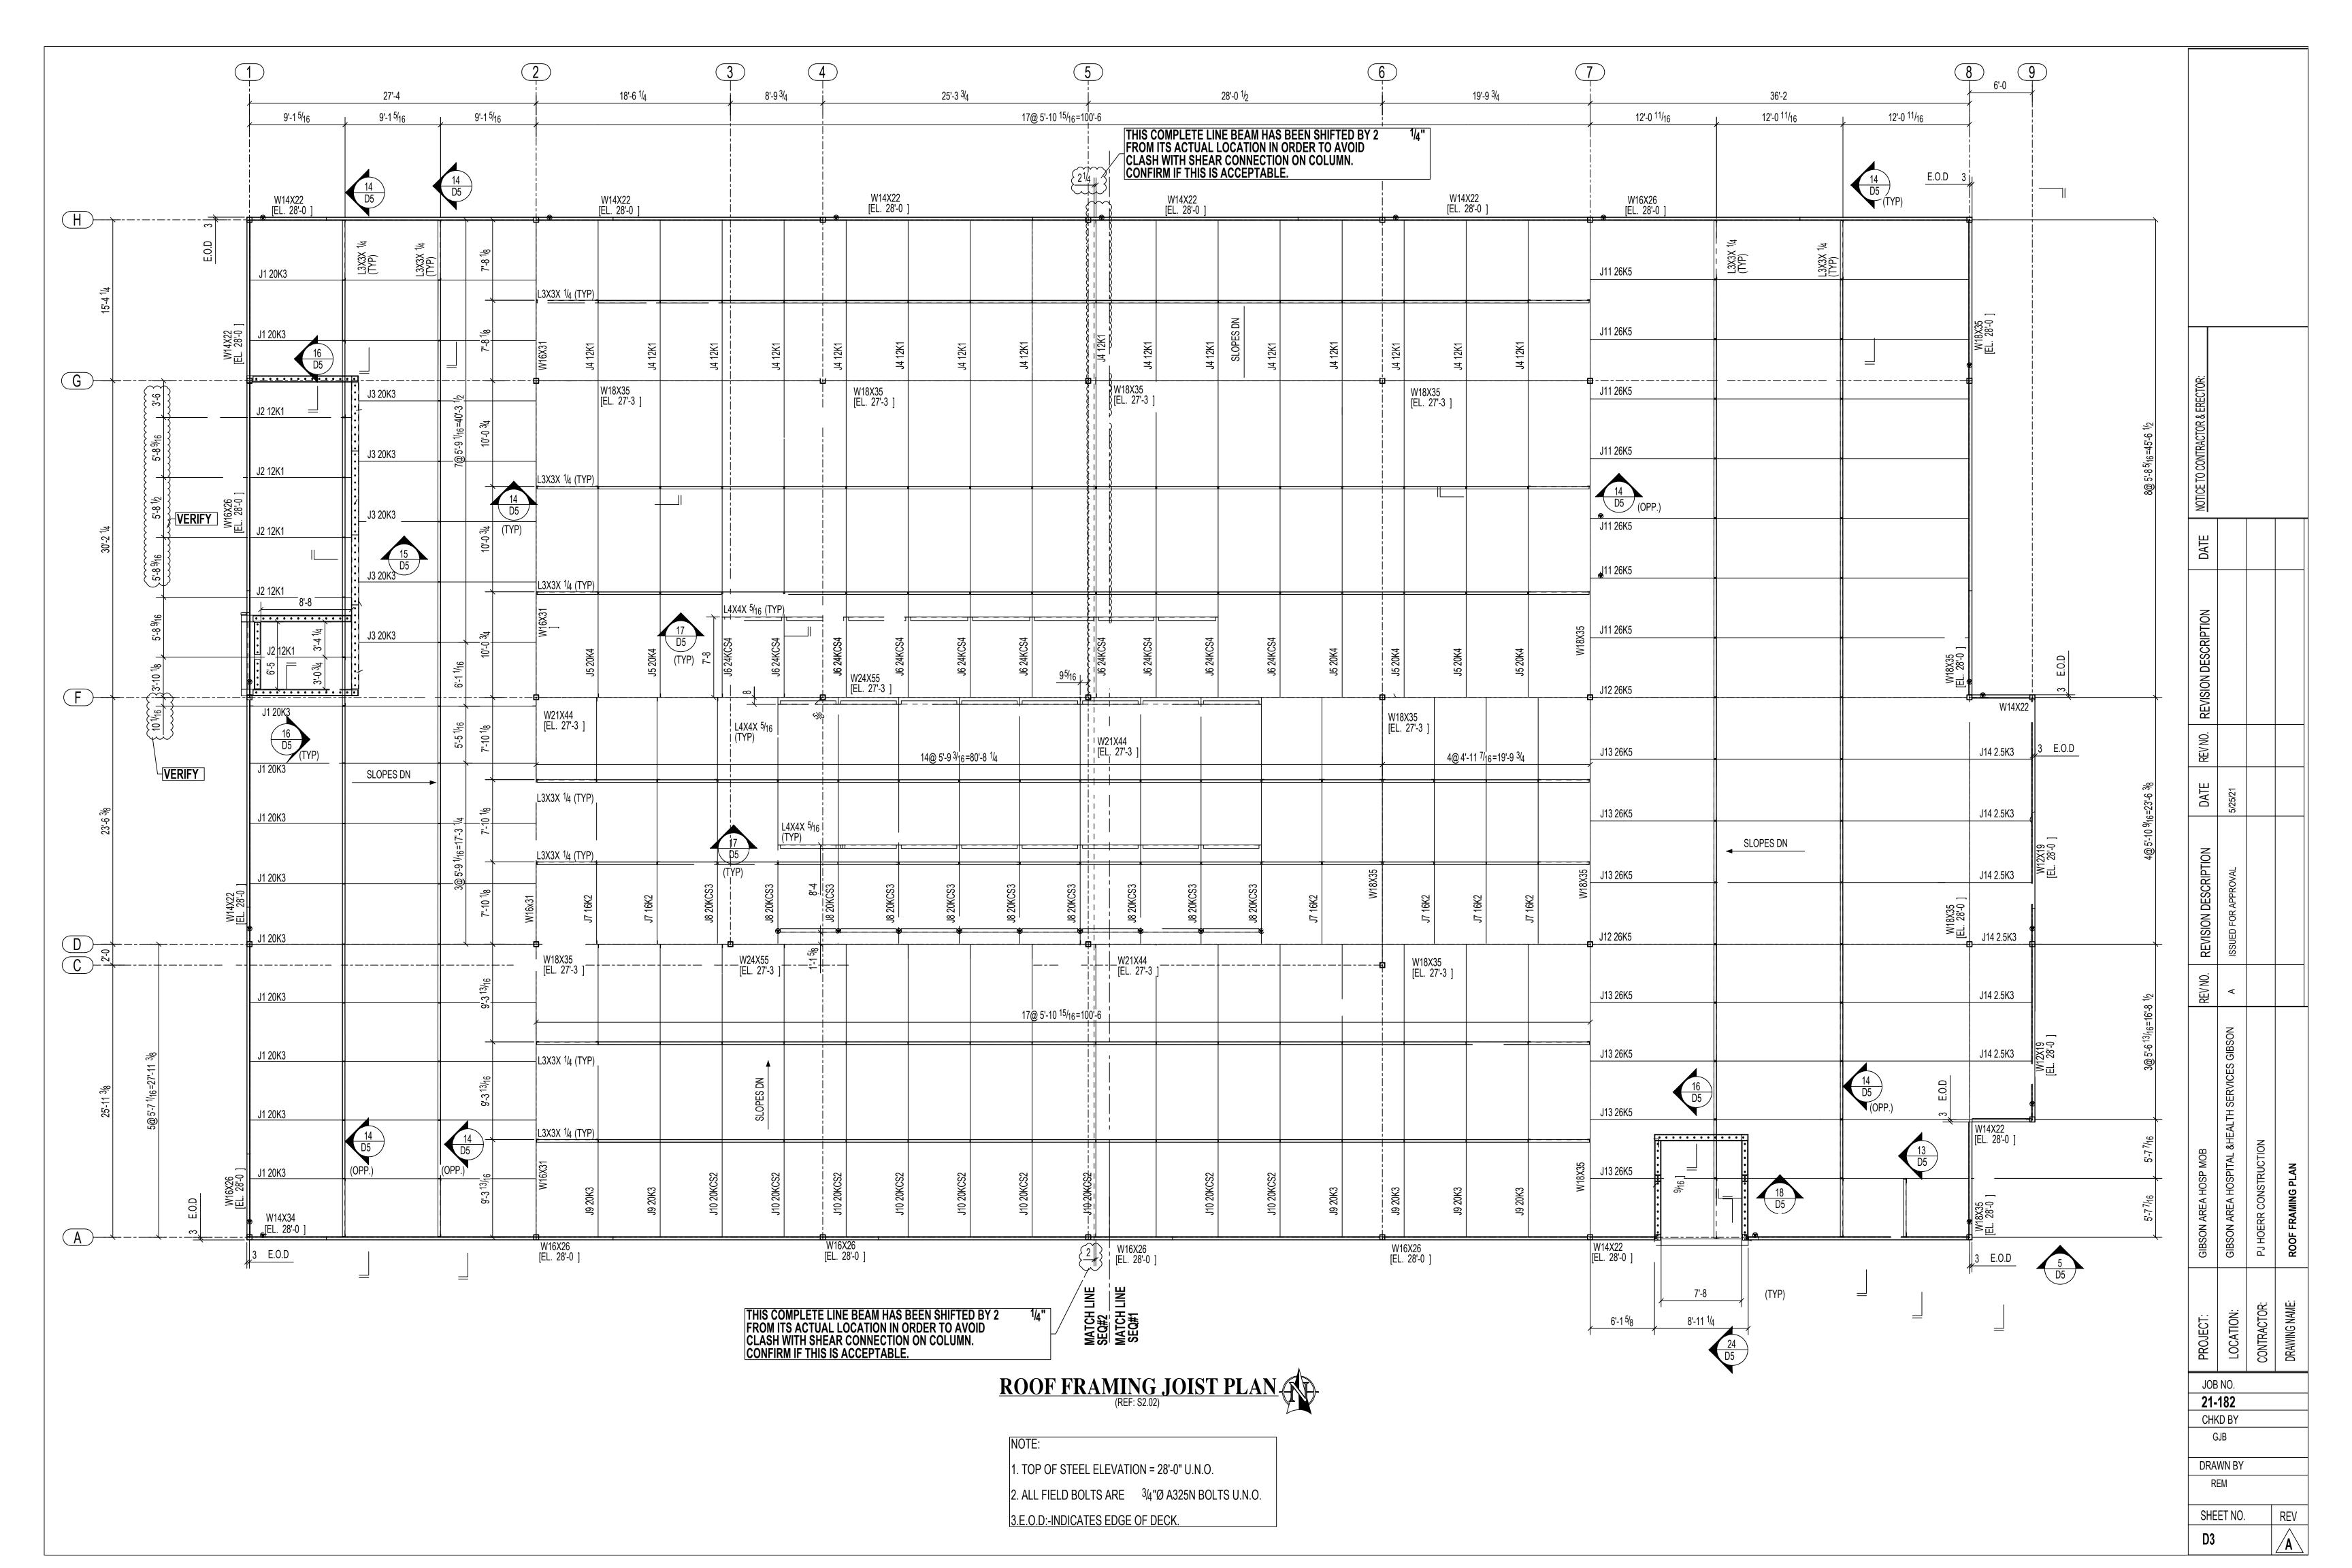

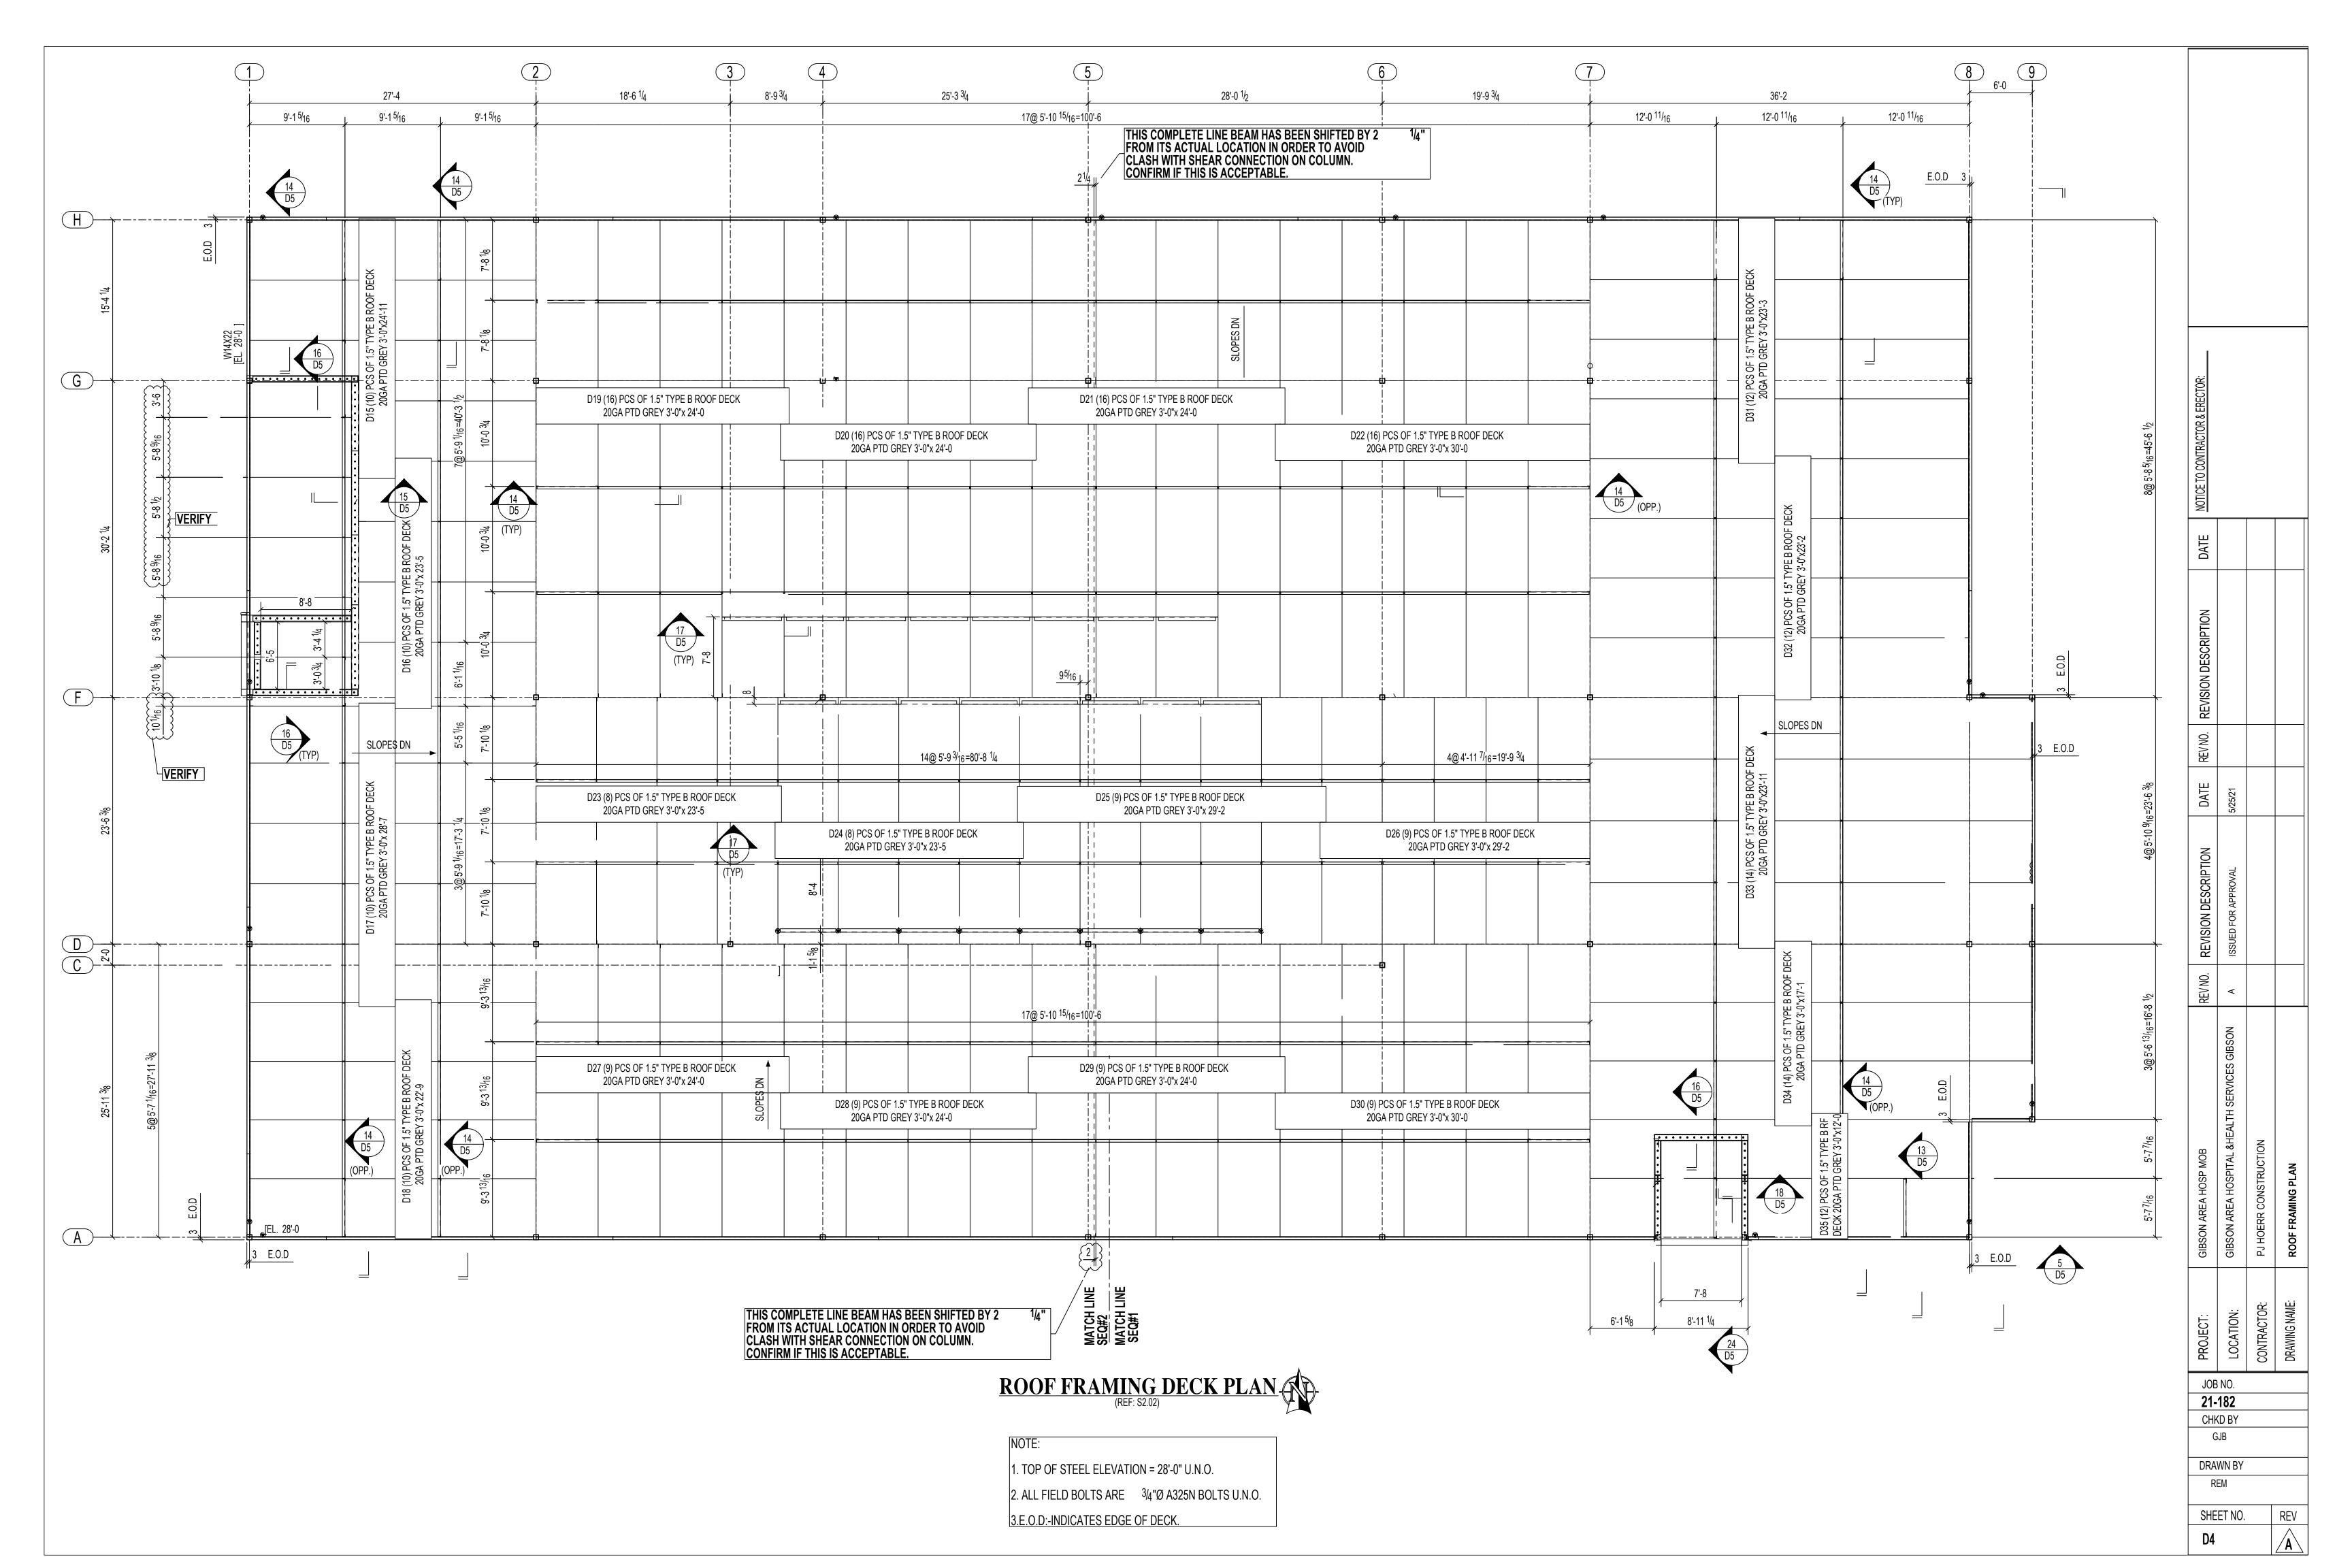

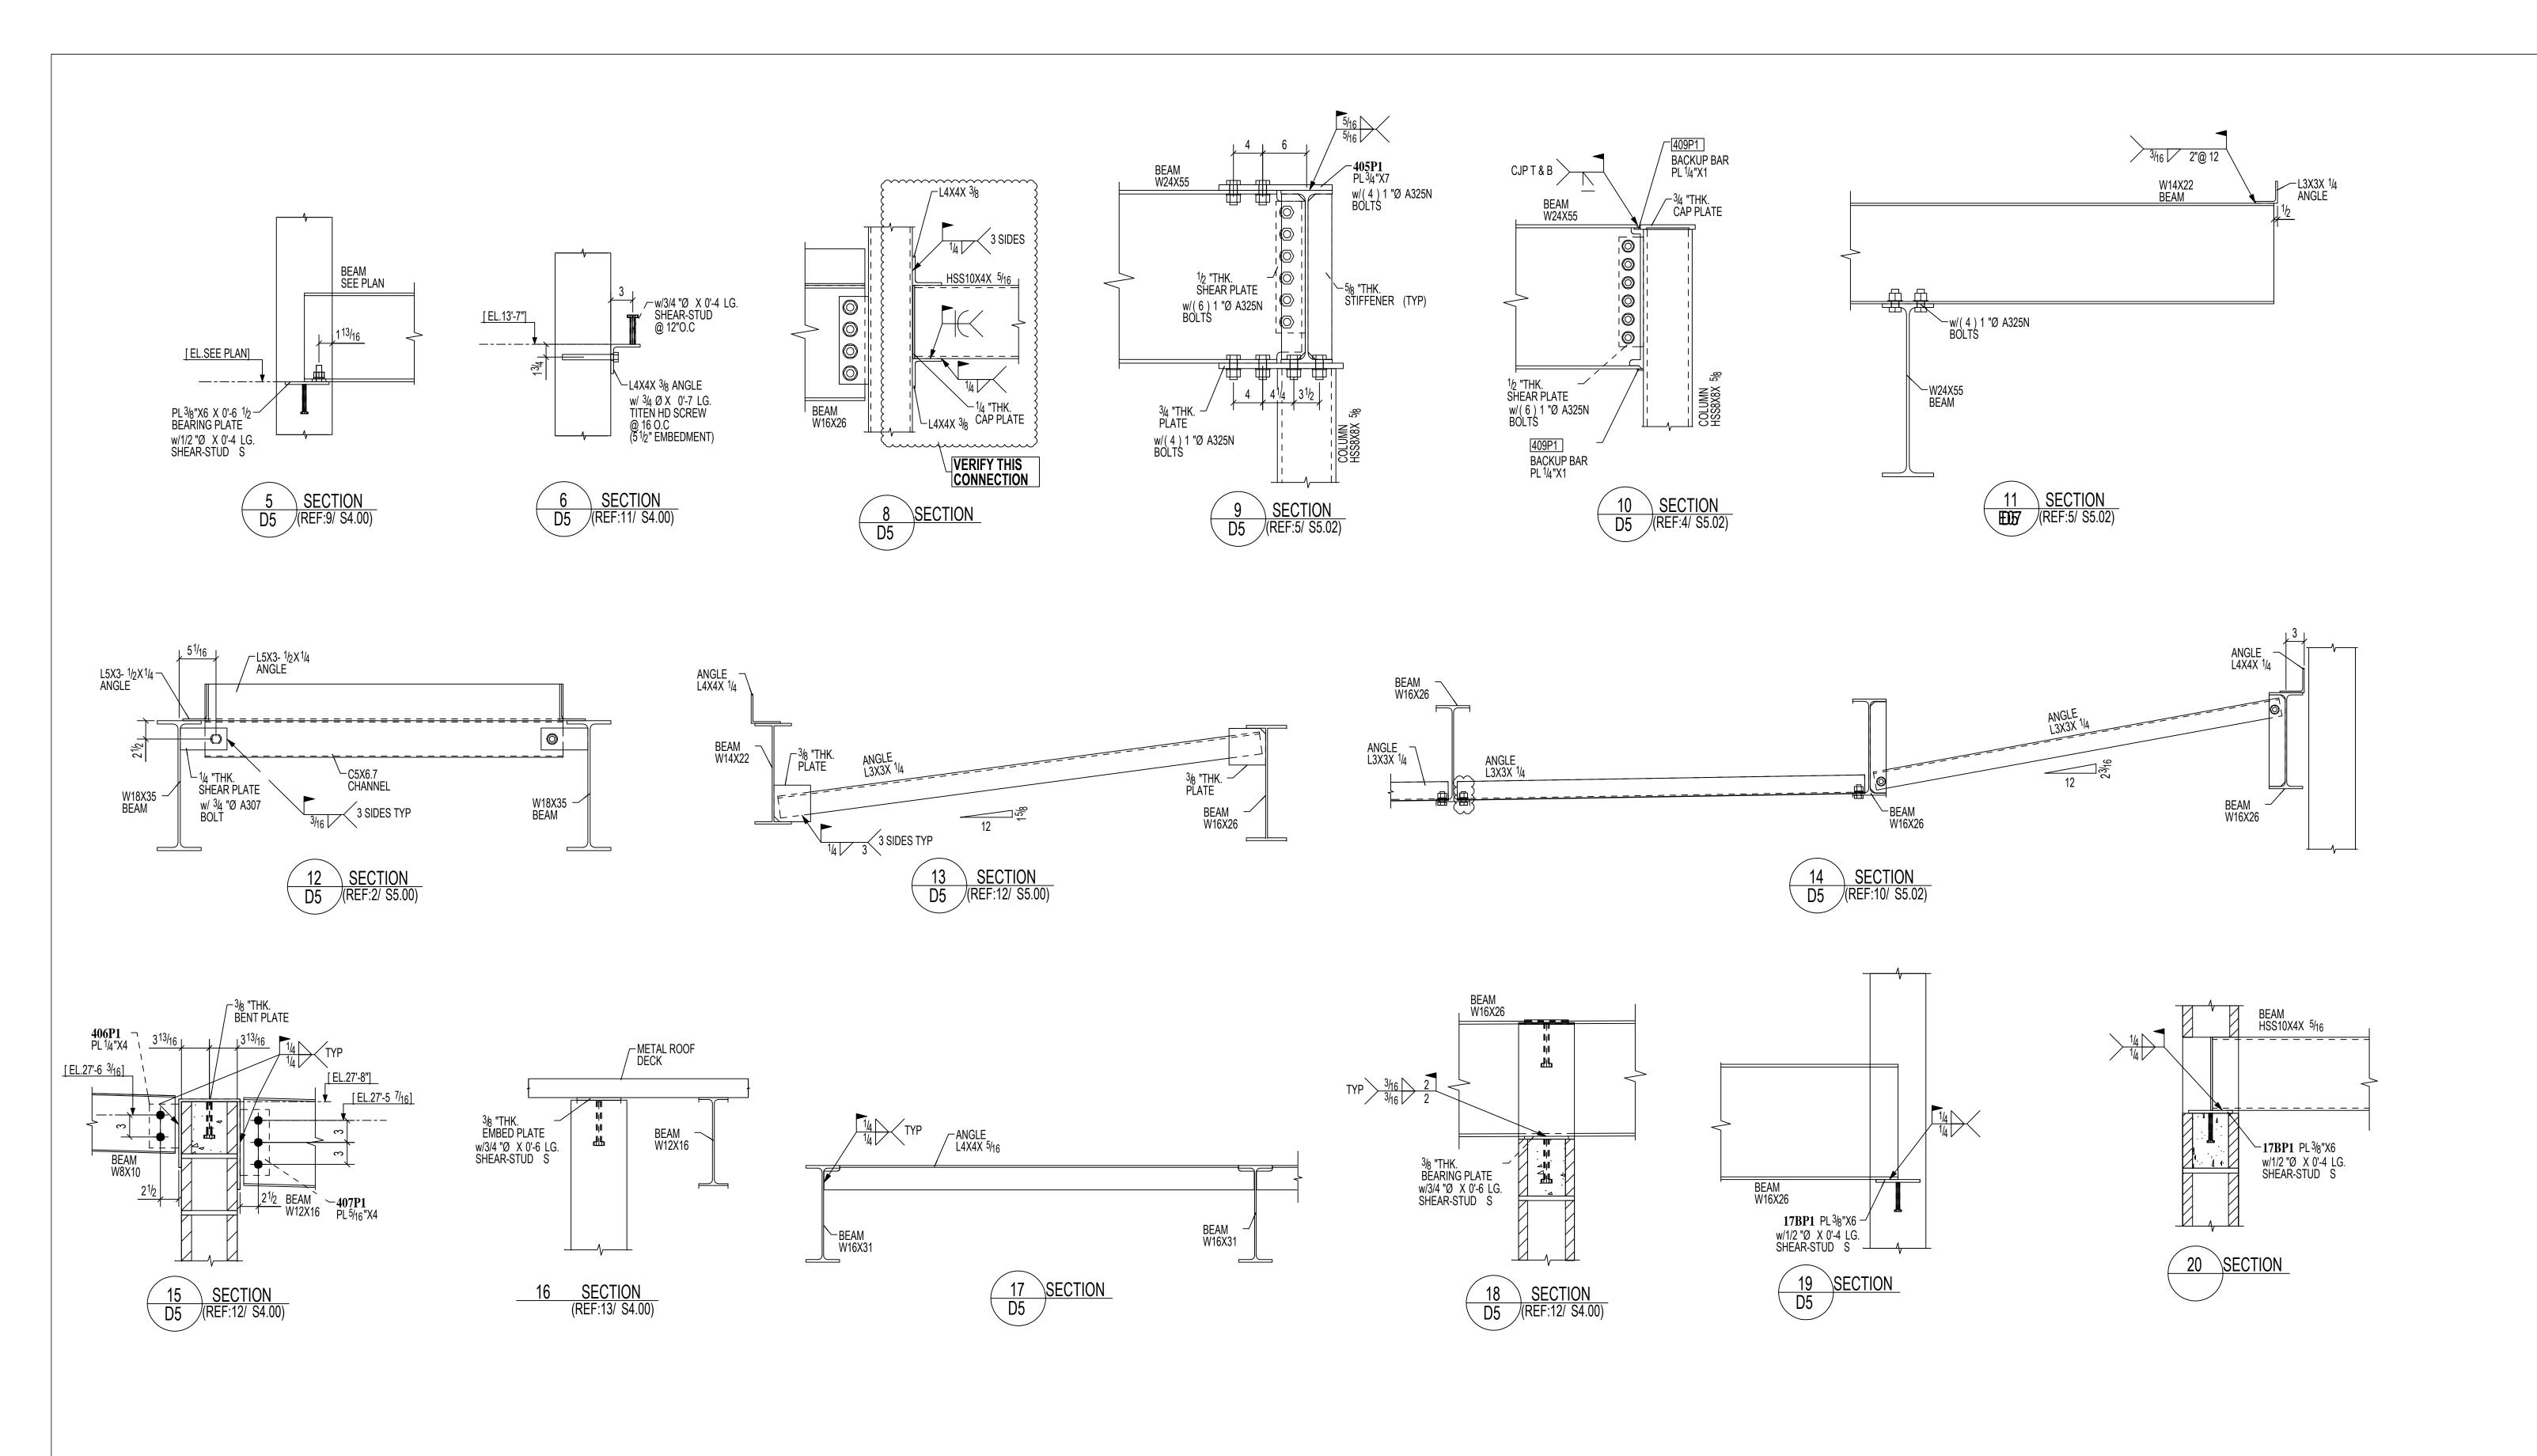

NOTICE TO CONTRACTOR & ERECTOR:			
DATE			
REV NO. REVISION DESCRIPTION			
DATE	5/25/21		
REV NO. REVISION DESCRIPTION	A ISSUED FOR APPROVAL		
GIBSON AREA HOSP MOB	GIBSON AREA HOSPITAL &HEALTH SERVICES GIBSON	PJ HOERR CONSTRUCTION	SECTIONS & DETAILS
PROJECT:	LOCATION:	CONTRACTOR:	DRAWING NAME:
JOB NO. 21-182 CHKD BY			
DRA	JB WN BY		
SHEET NO.  D5			REV A